



		DRAWN	MANPREET SINGH	CLIENT	UTTAR PRADESH EXPRESSWAYS INDUSTRIAL DEVELOPMENT AUTHORITY C-13, 2nd Floor, Parayan Bhawan, Vipin Khand, Gomti Nagar, Lucknow - 226010 (UP) Tel: 0522-4108184 / 2301492 / 2301142	INDEPENDENT ENGINEER:	DHHRUV CONSULTANCY SERVICE LTD. JOINT-VENTURE ARTEFACT PROJECTS LTD. IN ASSOCIATION WITH GLOBAL INFRA SOLUTIONS #501, 5th Floor, Plot No. 67, Pujit Plaza, Palm Beach Road, Sector-16 CBD Belapur, Navi Mumbai - 400614	SAFETY CONSULTANT:	TO BE APPOINTED
		DESIGNED	VARUN SINGH	CONCESSIONAIRE:	UNNAO PRAYAGRAJ ROAD PRIVATE LIMITED Adani Corporate House, Shantigram, Nr. Vaishno Devi Circle, S.G. Highway, Khodiyar Ahmedabad, Gujarat 382421				
APPROVED	S.MANDAL	INDEPENDENT ENGINEER:	LEA ASSOCIATES SOUTH ASIA PVT. LTD., B-1/E-27, Mohan Cooperative Industrial Estate, Mathura Road, New Delhi-110044	EPC CONTRACTOR:	ADANI ROAD TRANSPORT LIMITED Adani Corporate House, Shantigram, Near Vaishnodevi Circle, S.G. Highway, Ahmedabad-382421, Gujarat, India	EPC Sub Contractor	ITCem	ITD Cementation India Limited 9th Floor, Prima Bay, Tower-B, Gate No. 5, Sakhi Vihar Road, Powai, Mumbai 400 072	
PROOF CONSULTANT		PROJECT	DEVELOPMENT OF AN ACCESS CONTROLLED SIX LANE (EXPANDABLE TO EIGHT LANES) GREENFIELD "GANGA EXPRESSWAY" (GROUP IV, FROM KM 445+000 TO KM 601+847) IN THE STATE OF UTTAR PRADESH ON DBFOT (Toll) BASIS						
P.O.	26.10.2023	INITIAL SUBMISSION	TITLE:	GENERAL ARRANGEMENT DRAWING FOR MAJOR BRIDGE AT CH.530+138 (CA 530+123 Km.)					
REV. NO.	DATE	DESCRIPTION	DATE	REVISIONS	DRG. NO.:	73855LASAISTRMJBIGA-011530+138	(SHEET 2 OF 4)	REV. P0 SHEET-A2	

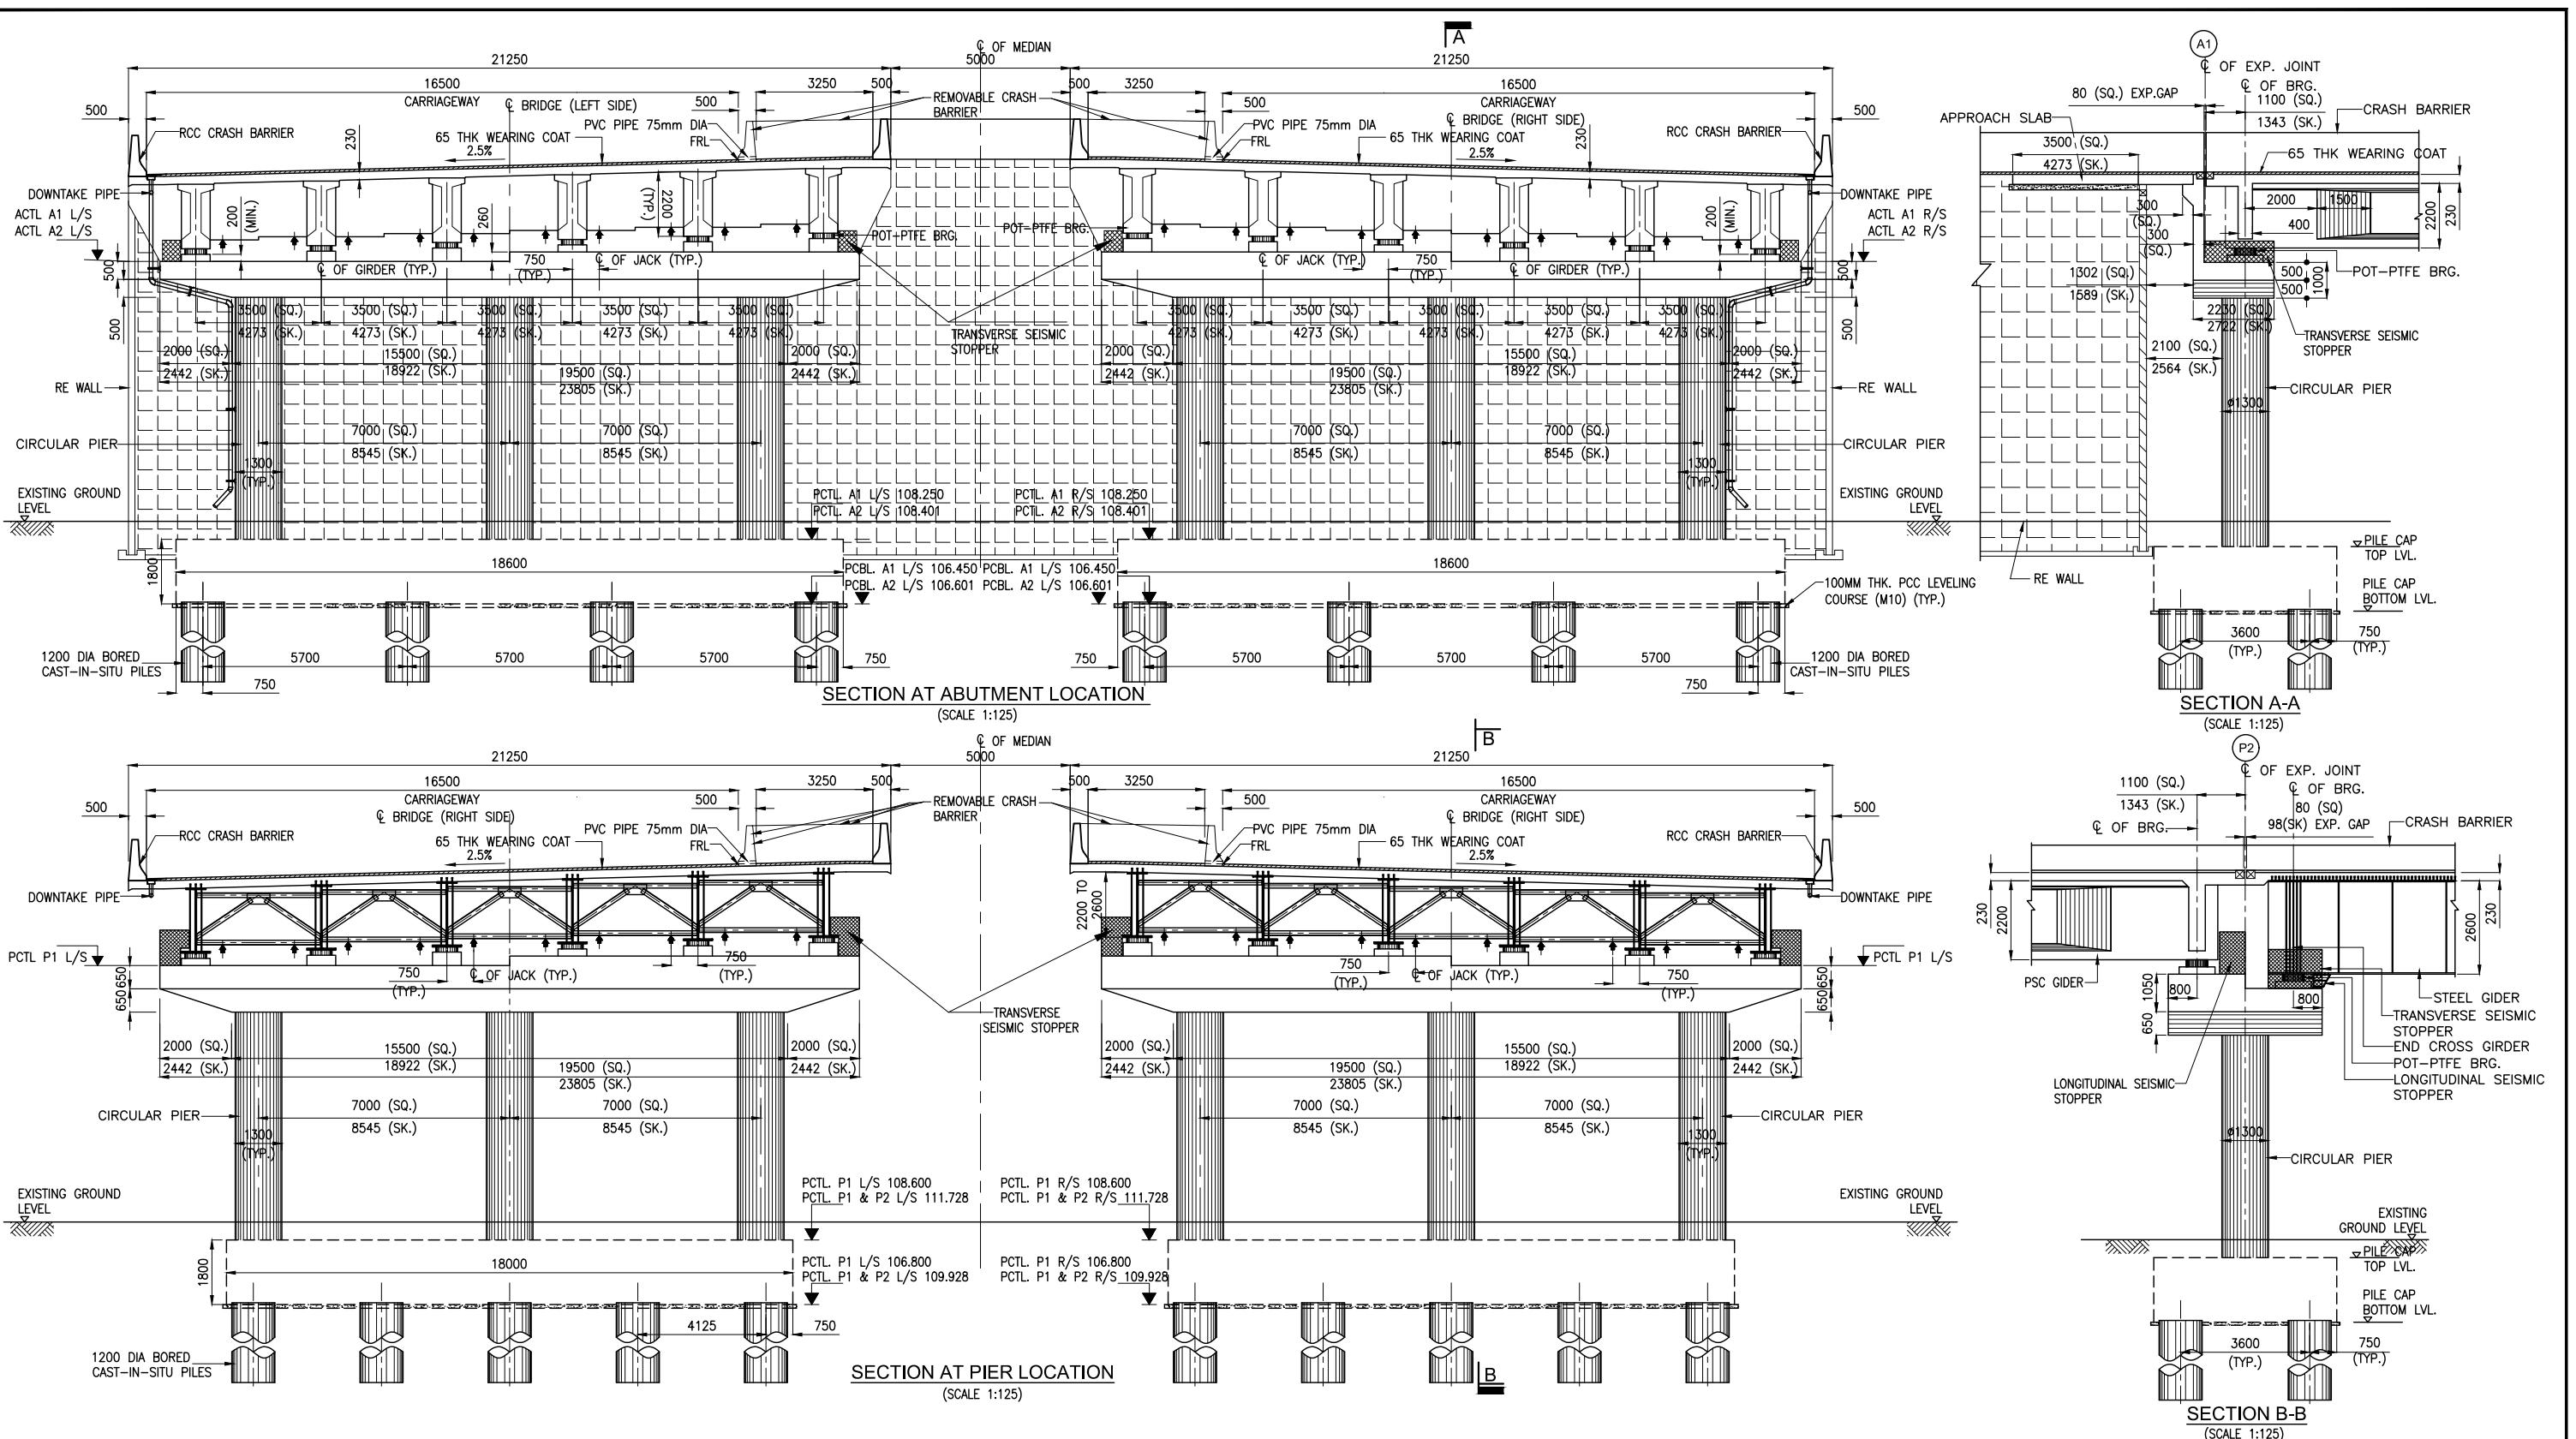


C.A. CH.	530+123
DESIGN CH.	530+138

NOTES:
READ THIS DRAWING IN CONJUNCTION WITH OTHER SHEETS OF THE SAME DRAWING NUMBER

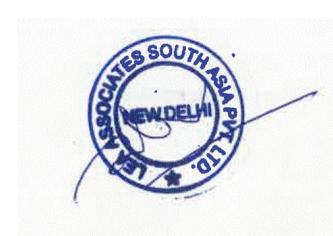

DRAWN	Manpreet Singh MANPREET	CLIENT	Uttar Pradesh Expressways Industrial Development Authority C-13, 2nd Floor, Parayan Bhawan, Vipin Khand, Gomti Nagar, Lucknow - 226010 (UP) Tel: 0522-4108184 / 2301492 / 2301142
DESIGNED	Varun Singh VARUN SINGH	CONCESSIONNAIRE	UNNAO PRAYAGRAJ ROAD PRIVATE LIMITED Adani Corporate House, Shantigram, Nr. Vaishno Devi Circle, S.G. Highway, Khodiyar Ahmedabad, Gujarat 382421
APPROVED	S. Mandal S.MANDAL	INDEPENDENT ENGINEER	DHRUV CONSULTANCY SERVICE LTD. JOINT-VENTURE ARTEFACT PROJECTS LTD. IN ASSOCIATION WITH GLOBAL INFRA SOLUTIONS #501, 5th Floor, Plot No. 67, Pujit Plaza) Palm Beach Road, Sector-16 CBD Belapur, Navi Mumbai-400614
PROOF CONSULTANT	LEA	EPC CONTRACTOR	ADANI ROAD TRANSPORT LIMITED Adani Corporate House, Shantigram, Near Vaishnodevi Circle, S.G. Highway, Ahmedabad-382421, Gujarat, India
INDEPENDENT ENGINEER		PROJECT	DEVELOPMENT OF AN ACCESS CONTROLLED SIX LANE (EXPANDABLE TO EIGHT LANES) GREENFIELD "GANGA EXPRESSWAY" (GROUP IV, FROM KM 445+000 TO KM 601+847) IN THE STATE OF UTTAR PRADESH ON DBFO (Toll) BASIS
		TITLE	GENERAL ARRANGEMENT DRAWING FOR MAJOR BRIDGE AT CH.530+138 (CA 530+123 Km.)
REV. NO.	DATE	DESCRIPTION	SCALE
P0	26.10.2023	INITIAL SUBMISSION	AS SPECIFIED
REVISIONS		DATE	REV. P0 SHEET-A2
		SEP. 2023	
			(SHEET 3 OF 4)
			DRG. NO.: 73855LASA1STRIMJBRIGA-01530+138

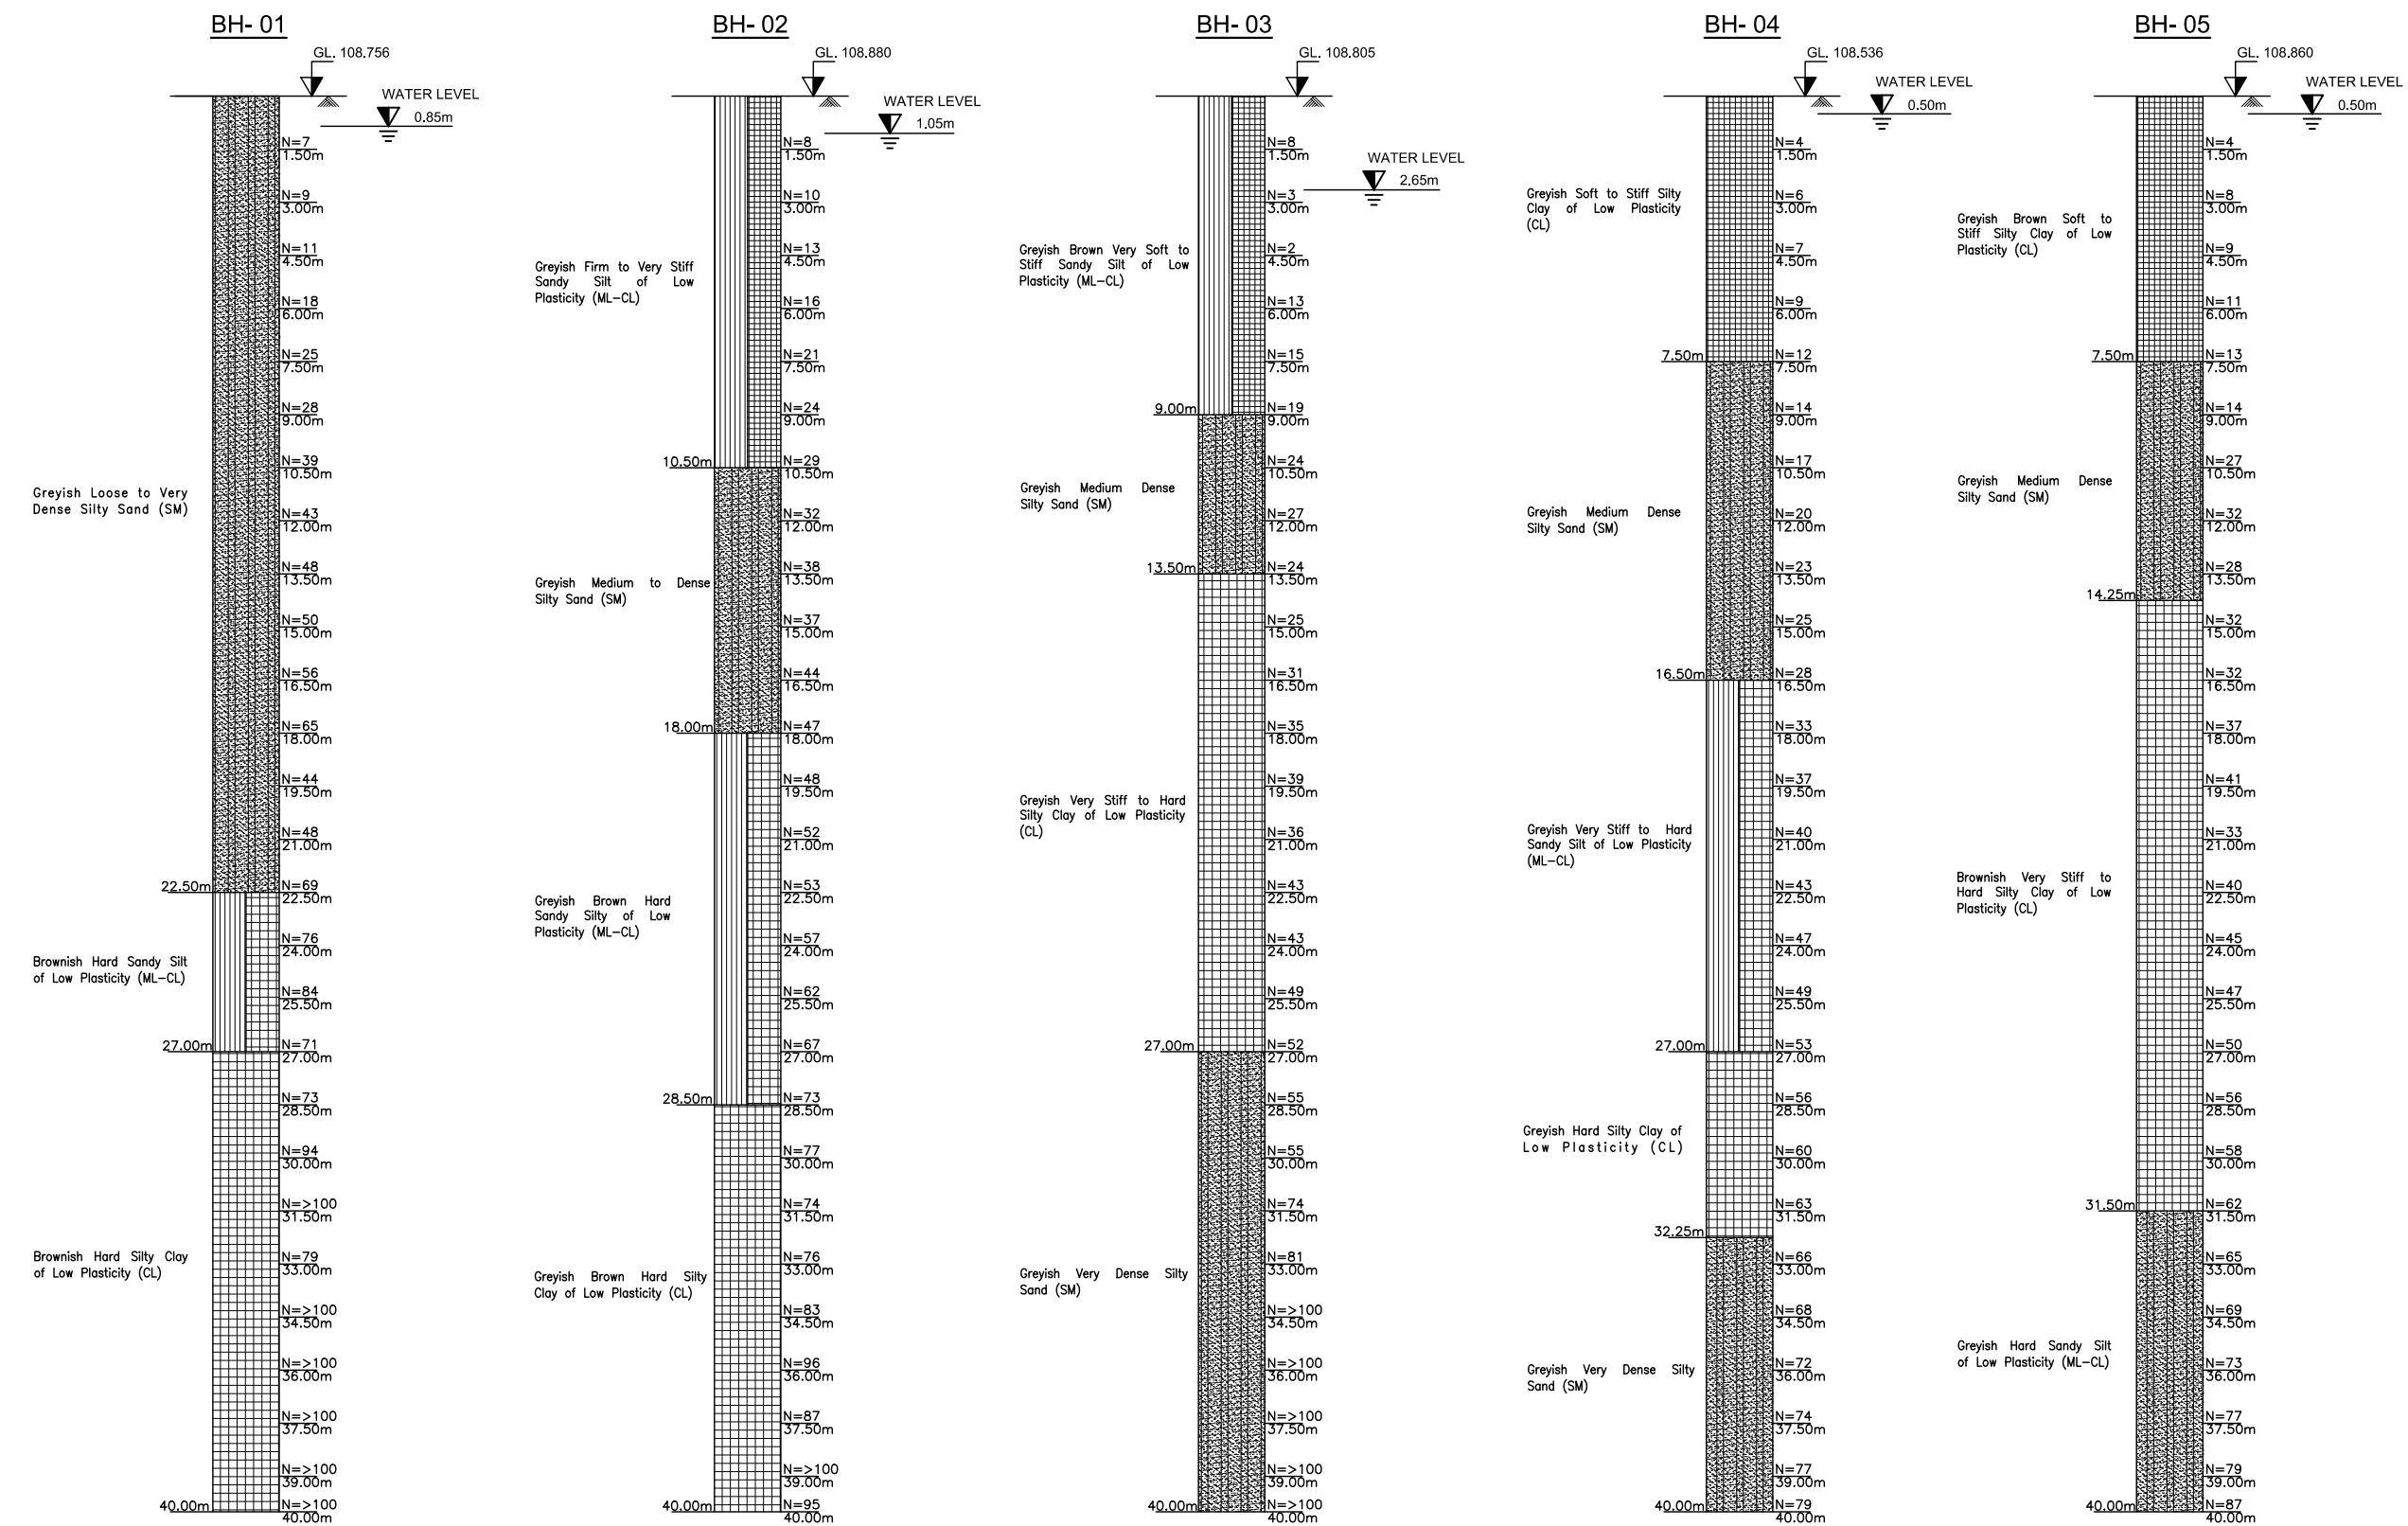


BORELOG DETAILS


REFERENCE DRAWINGS :

- GENERAL ARRANGEMENT DRAWING — 73855\LASA\STR\MJBR\GA-01\530+138 (SHEET 1 OF 3) & (2 OF 3)
- DETAILS OF TEST PILES FOR MJBR — 73855\LASA\530+138\MJBR\MCW\TP-02

C.A. CH.	530+123
DESIGN CH.	530+138

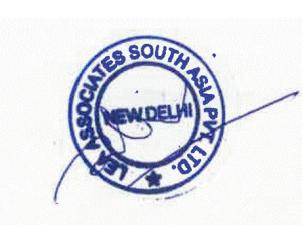

	DRAWN	KUNAL	CLIENT UPeida C-13, 2 nd Floor, Parayan Bhawan, Vipin Khand, Gomti Nagar, Lucknow - 226010 (UP) Tel: 0522-4108184 / 2301492 / 2301142	CONCESSIONNAIRE : UNNAO PRAYAGRAJ ROAD PRIVATE LIMITED Adani Corporate House, Shantigram, Nr. Vaishno Devi Circle, S.G. Highway, Khodiyar Ahmedabad, Gujarat 382421 INDEPENDENT ENGINEER : DHRUV CONSULTANCY SERVICE LTD. JOINT-VENTURE ARTEFACT PROJECTS LTD. IN ASSOCIATION WITH GLOBAL INFRA SOLUTIONS #501, 5th Floor, Plot No. 67, Pujit Plaza) Palm Beach Road, Sector-16 CBD Belapur, Navi Mumbai-400614 DESIGN CONSULTANT : LEA ASSOCIATES SOUTH ASIA PVT. LTD., B-1/E-27, Mohan Cooperative Industrial Estate, Mathura Road, New Delhi-110044 EPC CONTRACTOR : adani ADANI ROAD TRANSPORT LIMITED Adani Corporate House, Shantigram, Near Vaishnodevi Circle, S G Highway, Ahmedabad-382421, Gujarat, India EPC Sub Contractor : IT Cem ITD Cementation India Limited 9th Floor, Prima Bay, Tower-B, Gate No. 5, Sakhi Vihar Road, Powai, Mumbai 400 072 Contract Reliability & Quality
	DESIGNED	VARUN SINGH		
	APPROVED	S.MANDAL		
	PROOF CONSULTANT			
	INDEPENDENT ENGINEER			
	PROJECT		DEVELOPMENT OF AN ACCESS CONTROLLED SIX LANE (EXPANDABLE TO EIGHT LANES) GREENFIELD "GANGA EXPRESSWAY" (GROUP IV, FROM KM 445+000 TO KM 601+847) IN THE STATE OF UTTAR PRADESH ON DBFO (Toll) BASIS	
	TITLE :		GENERAL ARRANGEMENT DRAWING FOR MAJOR BRIDGE AT CH.530+138 (CA 530+123 Km.)	
	DRG. NO.:		73855\LASA\STR\MJBR\GA-01\530+138	
	REV. NO.	DATE	DESCRIPTION	SCALE AS SPECIFIED
			REVISIONS	(SHEET 4 OF 4) REV. R0 SHEET-A2

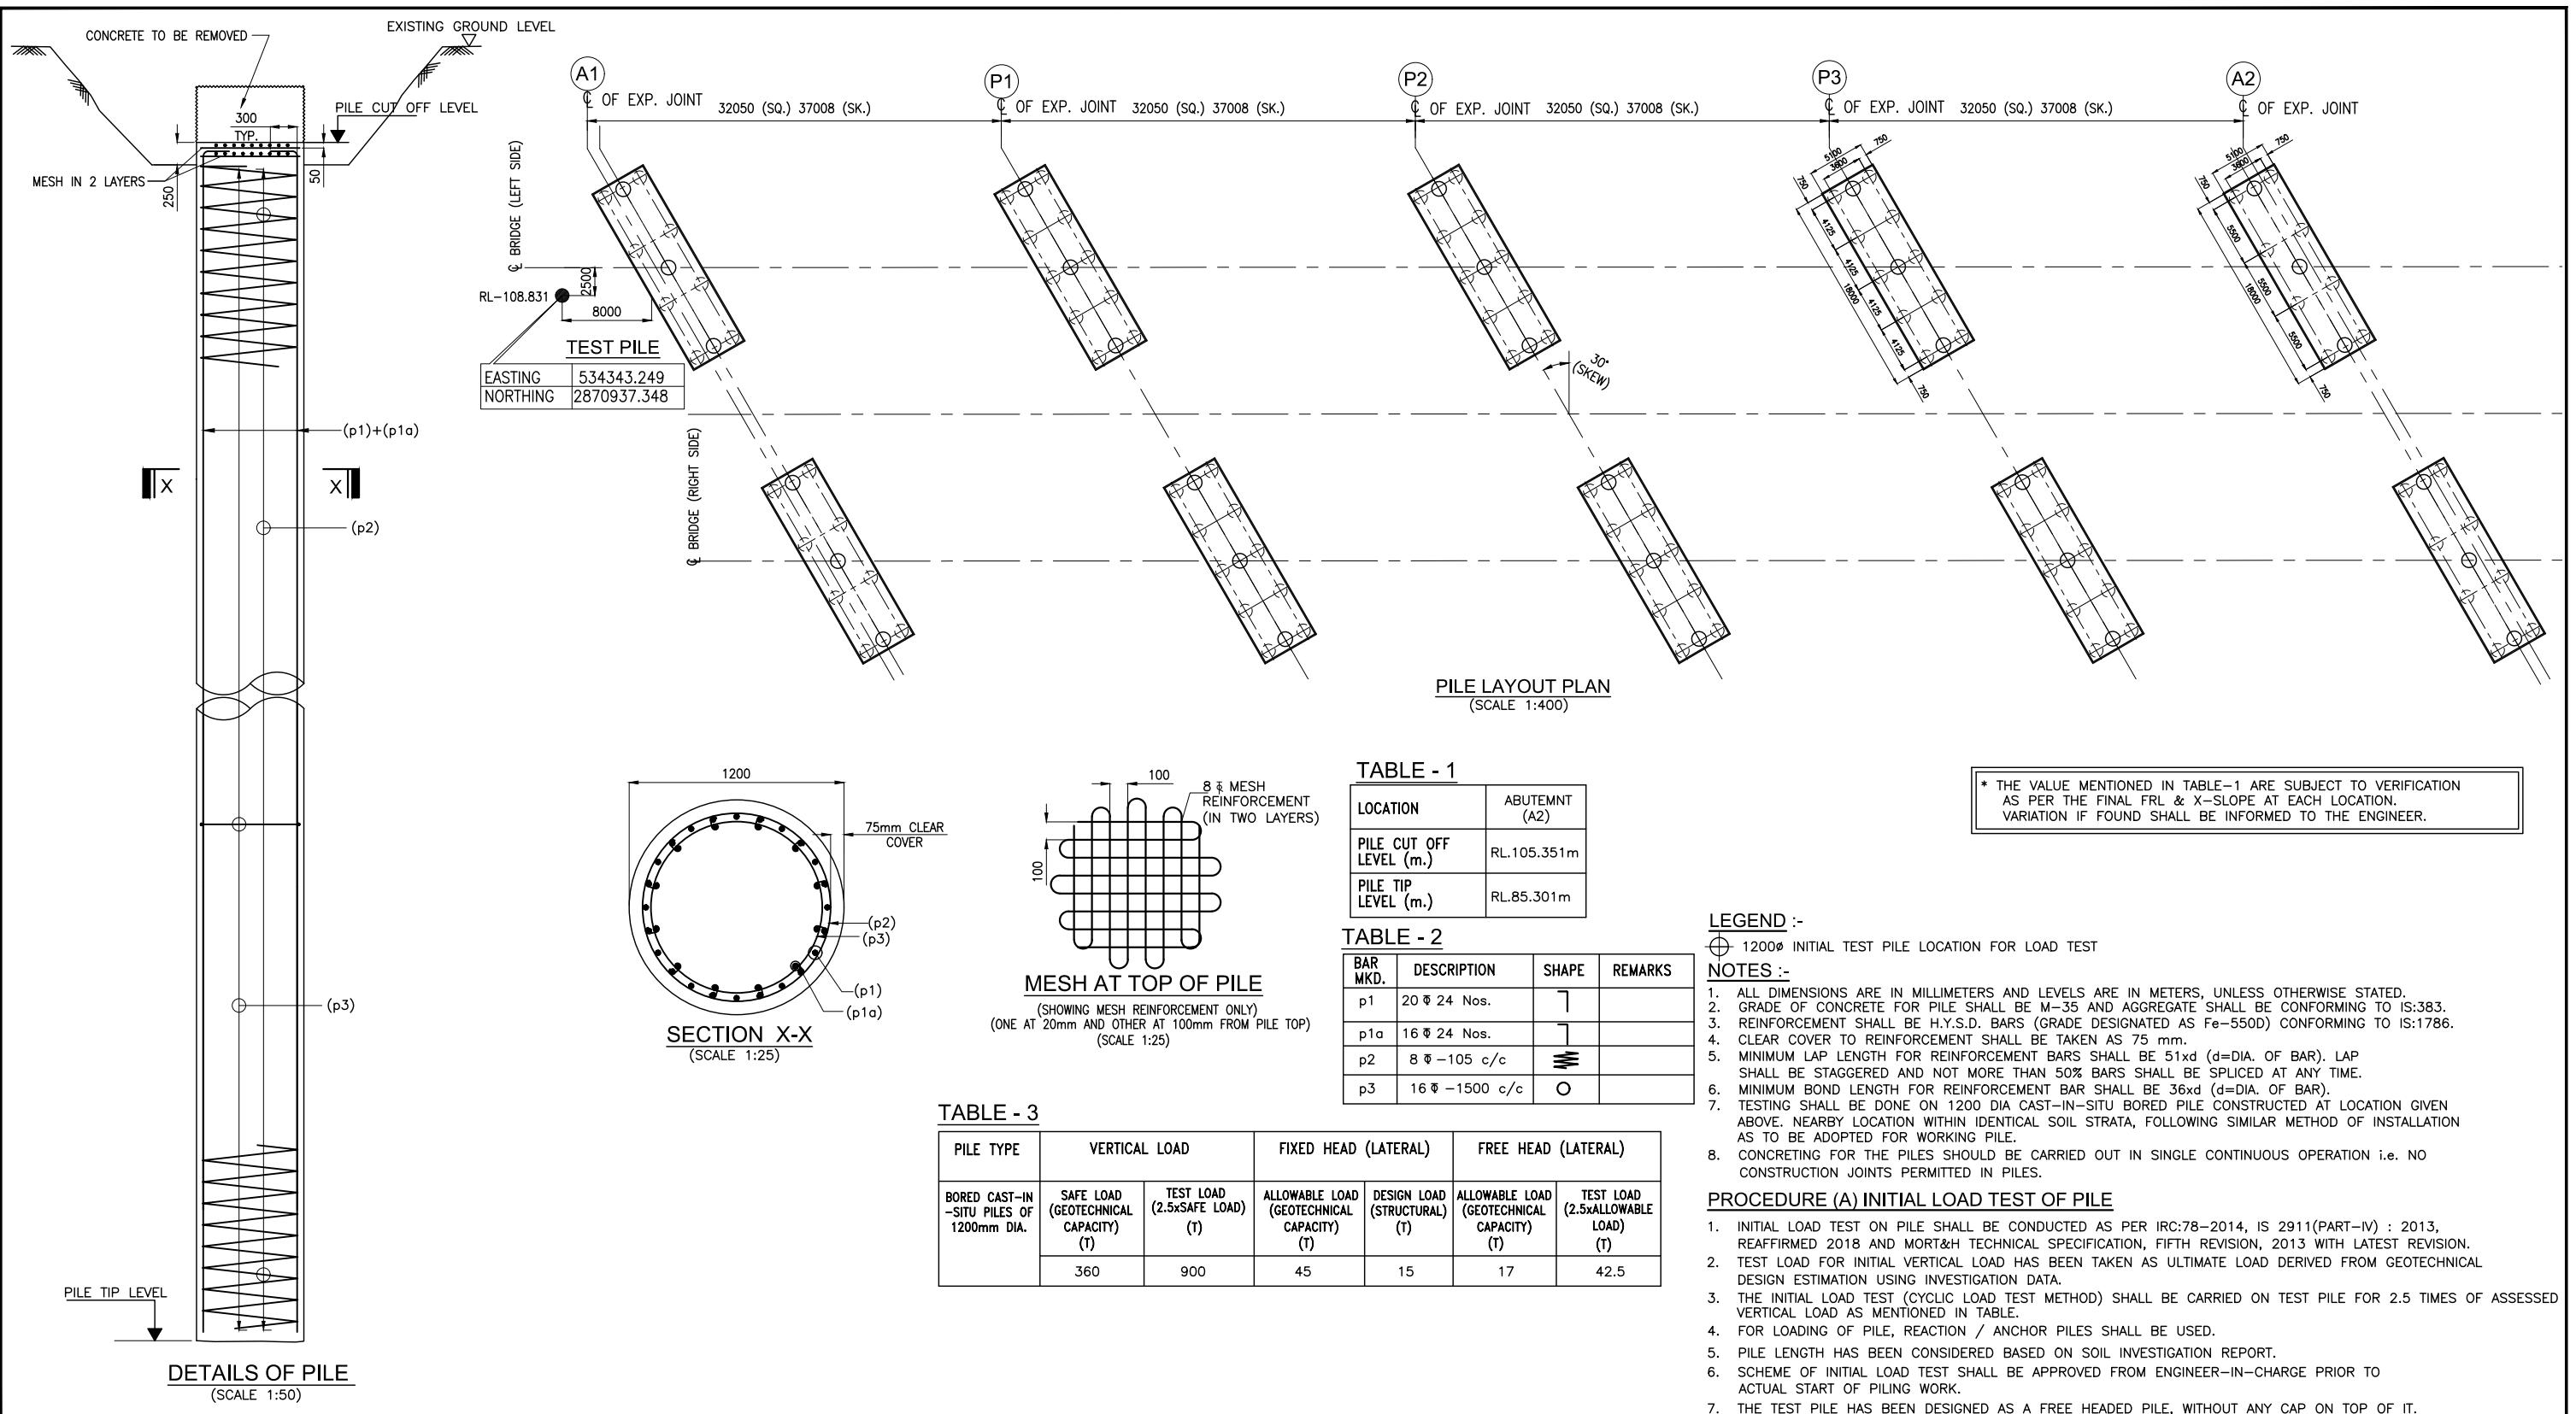

				DRAWN	KUNAL	CLIENT Uppeda UTTAR PRADESH EXPRESSWAYS INDUSTRIAL DEVELOPMENT AUTHORITY C-13, 2 nd Floor, Parayan Bhawan, Vipin Khand, Gomti Nagar, Lucknow - 226010 (UP) Tel: 0522-4108184 / 2301492 / 2301142		
		DESIGNED	VARUN SINGH	CONCESSIONNAIRE UNNAO PRAYAGRAJ ROAD PRIVATE LIMITED Adani Corporate House, Shantigram, Nr. Vaishno Devi Circle, S.G. Highway, Khodiyar Ahmedabad, Gujarat 382421	INDEPENDENT ENGINEER DHRUV CONSULTANCY SERVICE LTD, JOINT-VENTURE ARTEFACT PROJECTS LTD, IN ASSOCIATION WITH GLOBAL INFRA SOLUTIONS Dhruv Consultancy Services Ltd, Joint-Venture Artefact Projects Ltd, in Association with Global Infra Solutions #501, 5th Flr, Plot No. 67, Pujit Plaza) Palm Beach Road, Sector-16 CBD Belapur, Navi Mumbai-400614	SAFETY CONSULTANT : TO BE APPOINTED		
APPROVED	S.MANDAL	PROOF CONSULTANT		DESIGN CONSULTANT : LEA LEA ASSOCIATES SOUTH ASIA PVT. LTD., B-1/E-27, Mohan Cooperative Industrial Estate, Mathura Road, New Delhi-110044	EPC CONTRACTOR : adani ADANI ROAD TRANSPORT LIMITED Adani Corporate House, Shantigram, Near Vaishnodevi Circle, S.G. Highway, Ahmedabad-382421, Gujarat, India	EPC Sub Contractor ID Cem ID Cementation India Limited 9th Floor, Prima Bay, Tower-B, Gate No. 5, Sakhi Vihar Road, Powai, Mumbai 400 072		
INDEPENDENT ENGINEER		PROJECT	DEVELOPMENT OF AN ACCESS CONTROLLED SIX LANE (EXPANDABLE TO EIGHT LANES) GREENFIELD "GANGA EXPRESSWAY" (GROUP IV, FROM KM 445+000 TO KM 601+847) IN THE STATE OF UTTAR PRADESH ON DBFOT (Toll) BASIS					
REV. NO.	DATE	DESCRIPTION	DATE	SEP. 2023	TITLE : DETAILS OF TEST PILES FOR MJBR AT CH.530+138	DRG. NO. : 73855LASA1530+138MJBRMCWTP-02	SCALE : AS SPECIFIED	
REVISIONS		REVISIONS			REV. R0	SHEET-A2		